


C:\WORK\PROJECTS\SAUDI ARAMCO\GRP 126\PIR\126-SS7-PIP-ENG-DG-0008

THIS DRAWING AND DESIGN IS THE PROPERTY OF LAT MODULAR FABRICATION YARD LLC. AND MUST NOT BE COPIED OR LENT WITHOUT THEIR PERMISSION IN WRITING


CHECK THE REV. WITH THE LATEST DIN BEFORE USE
ALL DIMENSIONS ARE IN mm, UNLESS OTHERWISE SPECIFIED.

DO NOT SCALE, IF IN DOUBT ASK

THIS DRAWING MUST NOT BE USED FOR CONSTRUCTION
UNTIL SPECIFICALLY CERTIFIED FOR THAT PURPOSE UNDER AN ISSUE

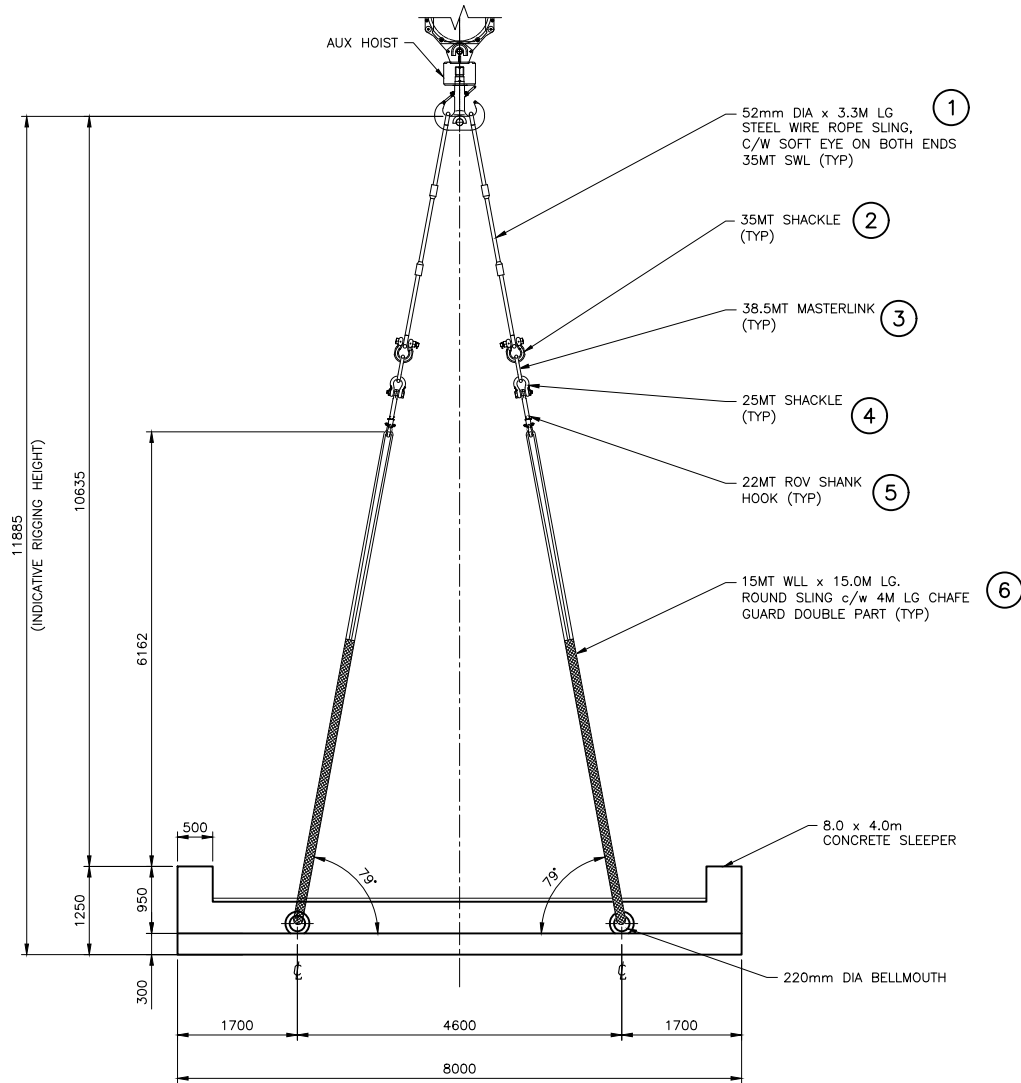

SIDE ELEVATION

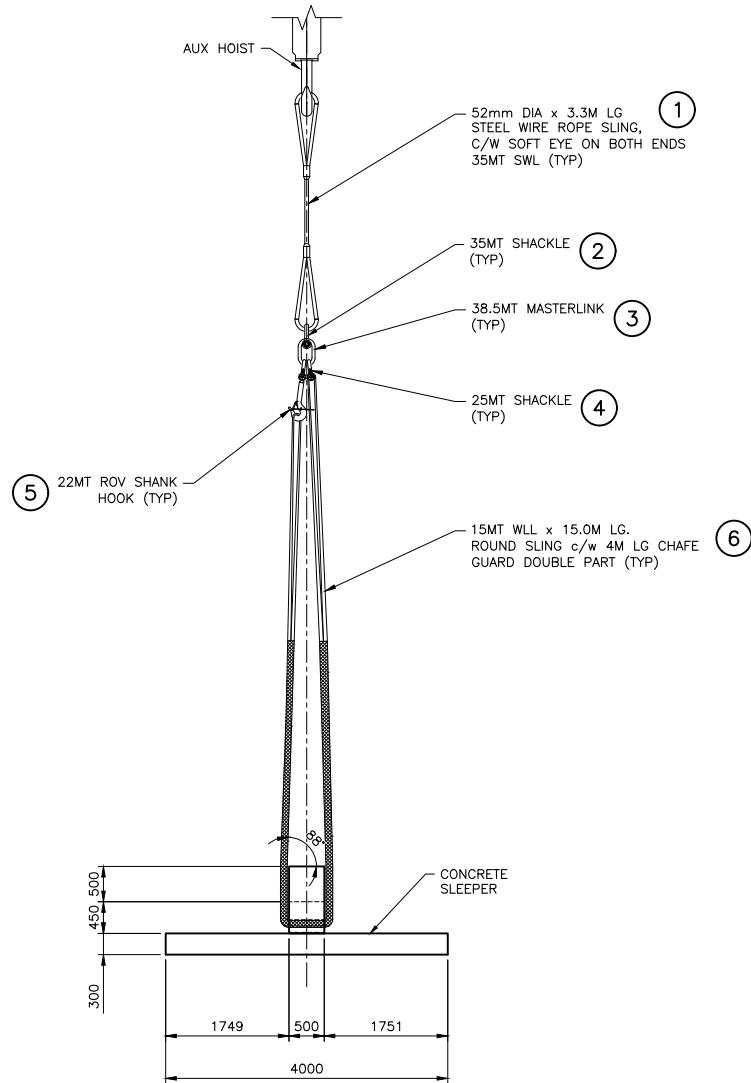

ELEVATION

OFFSHORE INSTALLATION RIGGING ARRANGEMENT FOR
6 x 3.0m AND 8 x 4.0m CONCRETE SLEEPERS (EXCLUDING TYPE CS8-1900)

SCALE = 1:50

(THE HEAVIEST 8 x 4.0m SLEEPER SHOWN FOR REPRESENTATION PURPOSE)

RIGGING MATERIAL LIST (OFFSHORE INSTALLATION)

ITEM	DESCRIPTION	QTY	WLL (MT)	MBL (MT)	LENGTH (M)	WEIGHT/UNIT (KG/M) (KG)	TOTAL WEIGHT (KG)
1	52 DIA. LG STEEL WIRE ROPE, (SOFT EYE ON BOTH ENDS)	2	—	175	3.3	11.0	72.6
2	35MT CROSBY BOLT ANCHOR SHACKLE (G-2130) OR EQUIVALENT	2	35	—	—	23.7	47.4
3	38.5MT MASTERLINK CROSBY (A-342) OR EQUIVALENT	2	38.5	—	—	11.4	22.8
4	25MT GREEN PIN SHACKLE (G-4163) OR EQUIVALENT	4	25	—	—	14.0	56.0
5	22MT GREEN PIN ROV SHANK HOOK (P-6740) OR EQUIVALENT	2	22	—	—	22.0	44.0
6	15.0M LG, 15MT WLL ROUND SLING c/w 4M LONG CHAFE GUARD DOUBLE PART	2	15	—	15.0	51.4	102.8
TOTAL WEIGHT :							345.6

NOTES:

- ALL DIMENSIONS SHOWN IN MILLIMETERS U.N.O.
- ALL WIRE SLING LENGTHS ARE FROM BEARING POINT TO POINT (U.N.O).
- ALL SLINGS AND GROMMETS, ROPES, SHACKLES AND HOOKS TO PROOF LOADED AND CERTIFICATION TO BE PROVIDED.
- ALL RIGGING TO BE SUBJECTED TO QA/QC CHECK AT SUPPLIER'S YARD.
- PROTECT SHARP EDGE AT WIRE INTERFACES.
- ADDITIONAL RIGGING CAN BE USED AS REQUIRED AT DIVING SUPERVISOR & PROJECT ENGINEER DIRECTION.
- HEAVIEST 8m x 4m (1.25m HEIGHT)
CONCRETE SLEEPER WEIGHT DETAILS :—

WEIGHT IN AIR	36.22 MT
WEIGHT SUBMERGED IN WATER	20.63 MT

HEAVIEST 6m x 3m (2.2m HEIGHT)
CONCRETE SLEEPER WEIGHT DETAILS :—

WEIGHT IN AIR	30.31 MT
WEIGHT SUBMERGED IN WATER	17.26 MT
- SYNTHETIC SLINGS WILL BE BENDING AROUND THE RIGGING & STRUCTURE AS SHOWN IN THE DRAWING. SLING VENDOR TO BE RE-CONFIRM WLL/MBL OF SOFT SLINGS. AFTER ACCOUNTING BENDING/TERMINATION LOSSES, IF ANY.

REFERENCE DOCUMENTS / DRAWINGS

DOCUMENT TITLE	DOCUMENT No.
CROSSING SUPPORT DETAILS	CA-711065 (SHEET 006)

REV	DATE	DESCRIPTION	DRAWN BY	DESIGN BY	CHKD BY	APPD BY
00a	01/23/2025	ISSUED FOR INFORMATION	SFA	YSK	PJK	PKB
00	01/15/2025	ISSUED FOR INFORMATION	SFA	YSK	PJK	PKB

CONTRACTOR:	COMPANY:
subsea 7	أرامكو السعودية Saudi Aramco

PROJECT: CRPO-126_16" PIPELAY FROM MRJN TP-14 TO MRJN 620/629

TITLE:
SLEEPER LIFT RIGGING DRAWING
FOR 6m AND 8m SLEEPERS
(SHEET 1 OF 6)

SIZE A1	SCALE AS NOTED	DWG NO.: 126-SS7-PIP-ENG-DG-0008	SHT.: 001	REV.: 00a
---------	----------------	----------------------------------	-----------	-----------